
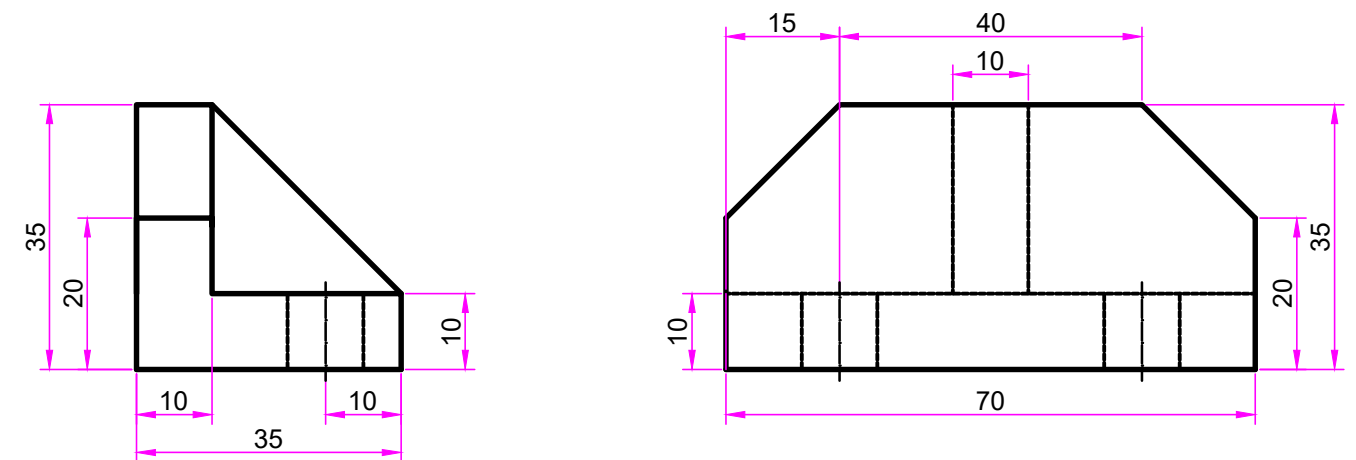


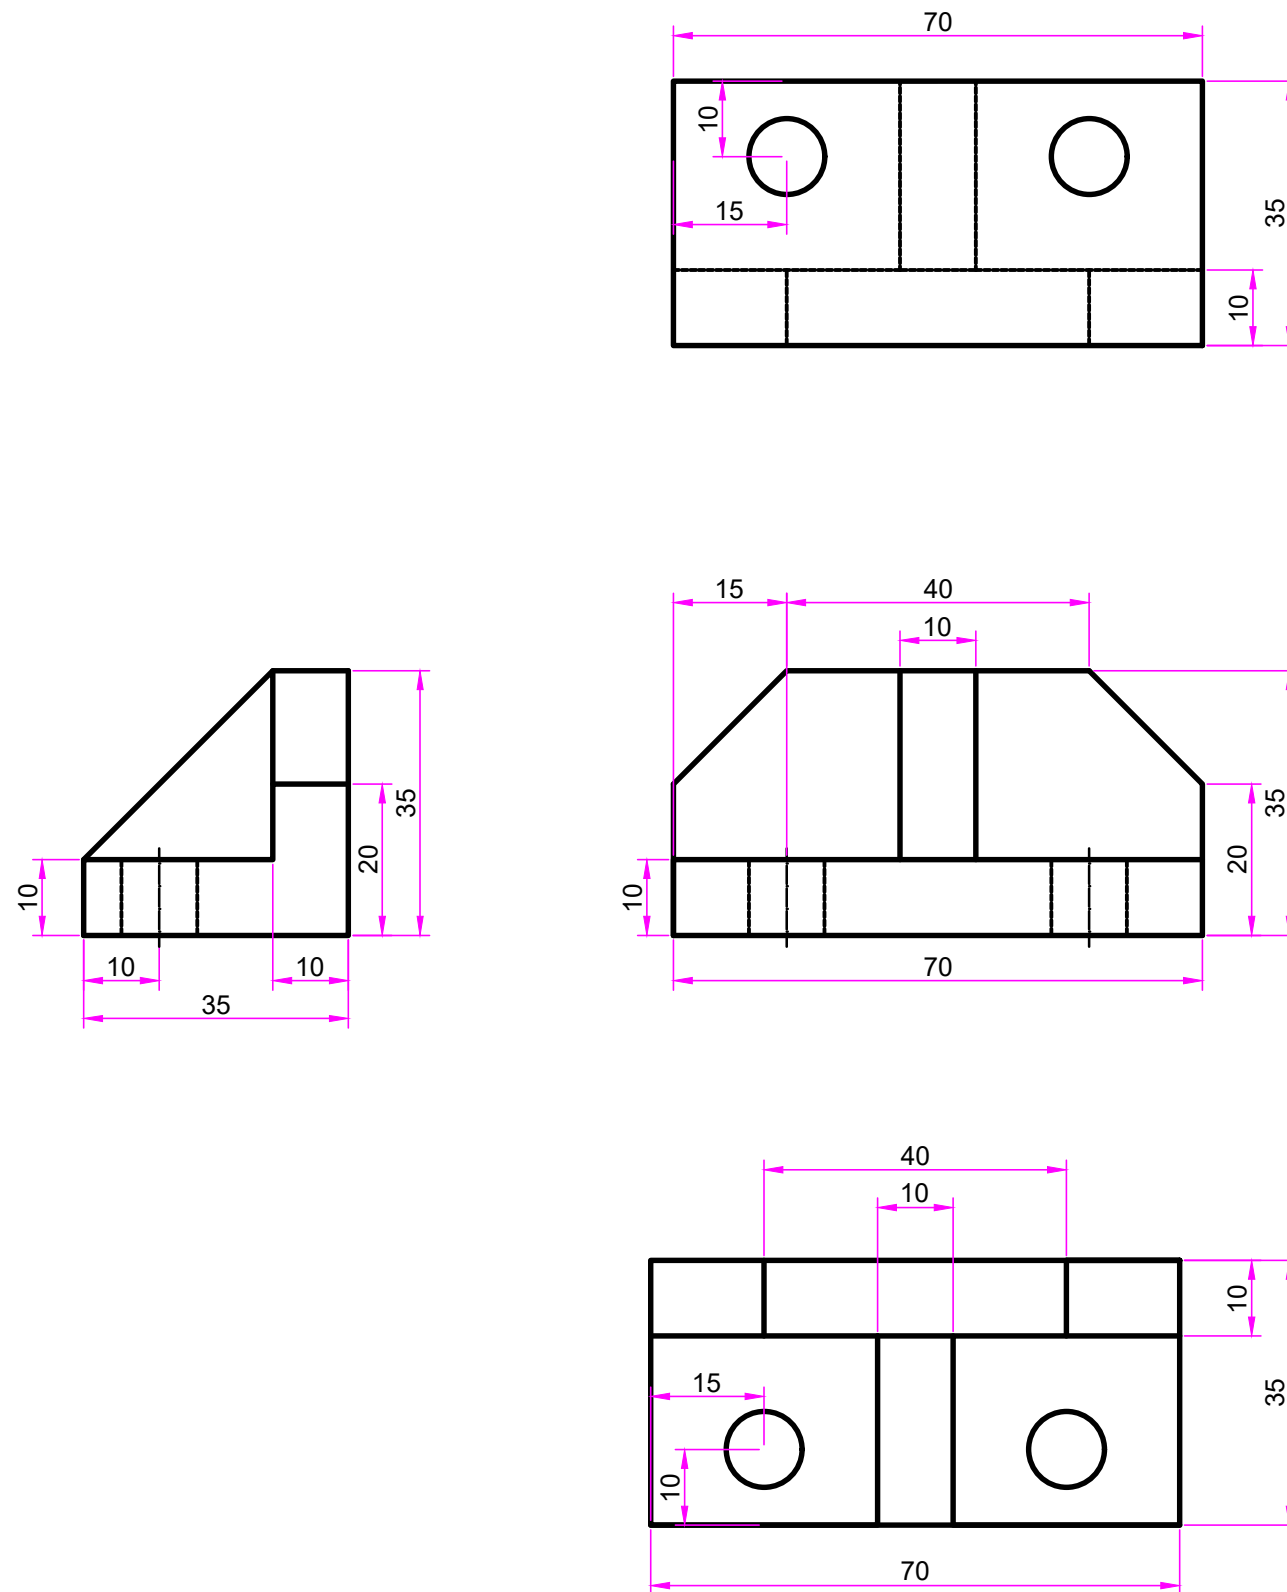

Τεχνικό Σχέδιο		Πανεπιστήμιο Θεσσαλίας			
Εργασία 1 - Μηχανολογικού Σχεδίου		ΗΜΜΗΥ			
ΣΚΑΡΠΙΔΗΣ ΚΩΝΣΤΑΝΤΙΝΟΣ		04592	2026	A3	